

[별첨 1] 지적측량결과도 작성 예시 목록 (지적업무처리규정 제25조제1항 관련)


1. 등록전환 측량결과도
2. 등록전환에 따른 임야분할측량결과도
3. 분할측량결과도 (600분의 1지역)
4. 분할측량결과도 (1200분의 1지역)
5. 분할측량결과도 (좌표)
6. 분할측량결과도 (좌표)
7. 경계복원측량결과도 (1200분의 1지역)
8. 경계복원측량결과도 (좌표)
9. 경계복원측량결과도 (좌표)
10. 지적확정측량결과도(경위의측량방법으로 세부측량을 한지역)
11. 지적전산화일에 의한 측량결과도(분할측량)
12. 지적전산화일에 의한 측량결과도(경계복원측량)

1. 등록전환 측량결과도



용인시 처인구 운학동 등록전환 측량결과도 제 123 호 (지적도 제 9 호) 축척 1200 분의 1
접수일 : 〇〇년 〇〇월 〇〇일 (〇〇 필)

(0.0)	신축량	용도지역
(0.0)	도락신축	〇〇〇지역
(0.0)	보정계수	1.0000

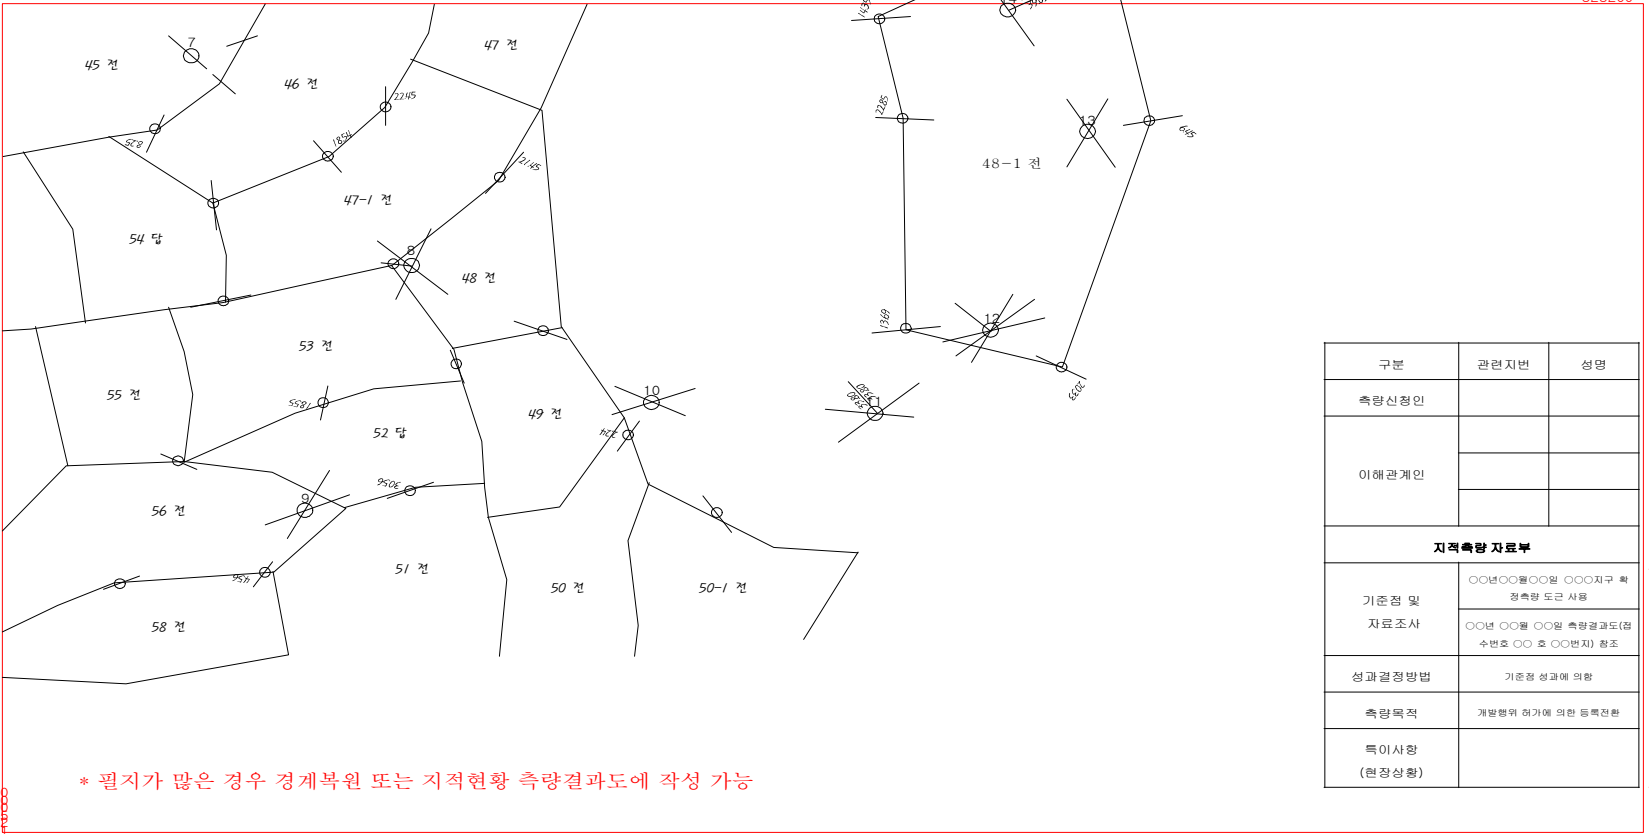

* 필지가 많은 경우 경계복원 또는 지적현황 측량결과도에 작성 가능

구분	관련지번	성명
측량신청인		
이해관계인		
지적측량 자료부		
기준점 및 자료조사	〇〇년 〇〇월 〇〇일 〇〇지구 확 정측량 도근 사용 〇〇년 〇〇월 〇〇일 측량결과도(접 수번호 〇〇 호 〇〇번지) 참조	
성과결정방법	기준점 성과에 의한	
측량목적	개발행위 허가에 의한 등록전환	
특이사항 (현장상황)		

지적측량 기준점 번호	거리	방위각	좌 표	
			X	Y
12			44399.00	20602.06
13	90 21	58-53-49	44399.00	20679.90
14	86 55	118-38-37	44399.00	20775.86

동리명	지번	측정 방법	회수 및 산출수		측정면적	도락신축 보정계수	보정면적	원면적	산출면적	결정면적	비고
운학	48-1	전자	제 1 회	제 2 회	155.736	155.736	155.736	155.736	155.736	155.736	
											측정 지적
											년 월 일
											검사 지적
											년 월 일
											〇

측량준비도	측량결과도	측량 성파도	도 면	
작성	확인	작성	확인	검사
작성	확인	작성	확인	검사
작성	확인	작성	확인	검사
작성	확인	작성	확인	검사
작성	확인	작성	확인	검사
작성	확인	작성	확인	검사
작성	확인	작성	확인	검사

기준점 번호 및 거리 방위각 좌표 기재

측정면적, 보정면적은 셋째자리, 산출면적은 경계점좌표등록부 지역,1/600 지역은 둘째자리,
그 밖의 지역은 첫째자리까지, 결정면적은 등록단위까지 입력

(0.0) 도파선축 (0.0)	신축량	용도지역
	mm	○○○지역
	보정계수	
	1.0000	



의적측량 기준 면	거리	방위각	좌		표	
			X	Y		
12	-	-	44398.00	201902.66		
13	90 21	58-53-49	44398.00	201979.90		
14	86 55	118-38-37	44398.00	201755.86		
	-	-	-	-	-	-
	-	-	-	-	-	-
	-	-	-	-	-	-
	-	-	-	-	-	-
	-	-	-	-	-	-

동리명	지번	측정 방법	회수 및 산출수		측정면적	도락신측 보정계수	보정면적	원면적	산출면적	결정면적	비고
			제 1 회	제 2 회							
운학	삼 3	전자	1274.375	1274.375	1274.375				1291.2	1291	
	삼 3-1	전자	155.736	155.736	155.736				157.8	158	
	삼 3				1490.111			1499	1499.0	1499	측정 지적 년 월 일 ⑩
											검사 지적 년 월 일 ⑩

측량준비도		측량결과도			측량 성확도 작성	도 면	
작성	확인	작성	확인	점사		정리	검사
측량 년 월 일						시 군 구	
		팀장 지적 팀원 지적 팀원 지적				⑪ ⑫ ⑬	
점사 년 월 일		지적				⑭	

측정면적, 보정면적은 셋째자리, 산출면적은 경계점좌표등록부 지역, 1/600 지역은 둘째자리, 그 밖의 지역은 첫째자리까지, 결정면적은 등록단위까지 입력


3. 분할측량결과도(600 분의 1 지역)

42750250240111271000139040420070431.dat



용인시 처인구 운학동 분할측량결과도 제 1123 호 (지적도제 10 호) 축척 600 분의 1
접수일 : 〇〇년 〇〇월 〇〇일 (〇〇 필)

(0.0)	신축량	용도지역
(0.0) 도락신축 (0.0)	mm 0.0	〇〇〇지역
(0.0)	보정계수	1.0000

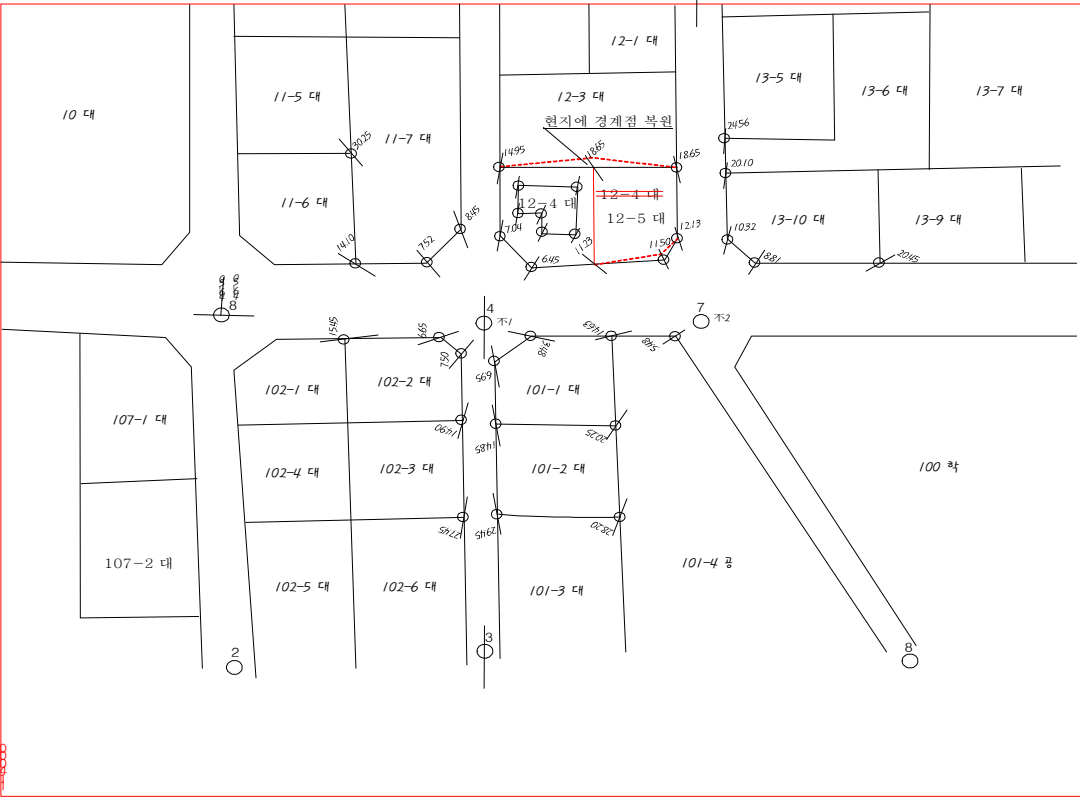

측정점위치설명도

표지종류	수량	번호	표지종류	수량	번호
비포장용			표지종류	2	1-2
필롯1호			표시후 미설치		
필롯2호					

구분	관련지번	설명
측량신청인		
이해관계인		

지적측량 자료부

기준점 및 자료조사	〇〇년 〇〇월 〇〇일 〇〇지구 학 점측량 도근 사용 〇〇년 〇〇월 〇〇일 측량결과도(점 수번호 〇〇 호 〇〇번지) 참조
성과결정방법	기준점 성과에 의함
측량목적	토지 매매를 위한 분할
특이사항 (현장상황)	

323000

예시임

322800

지적측량 기준점 번호	거리	방위각	좌표	X	Y
1	mm	° ° ' "	mm mm	443955.00	201912.08
2	90 21	58-53-49	mm mm	443955.00	201979.90
3	88 55	118-38-37	mm mm	443955.00	201755.88
	.	.	.	.	.
	.	.	.	.	.
	.	.	.	.	.
	.	.	.	.	.

동리 명	지번	측정 방법	회수 및 산출수		측정면적	도락신축 보정계수	보정면적	원면적	산출면적	결정면적	비고
			제 1 회	제 2 회							
			전자	전자							
관 내	12-4	전자	250.474	250.474	250.474				249.03	249.0	
	12-5	전자	253.632	253.632	253.632				252.17	252.2	
	12-4				504.106			501.2	501.20	501.2	
											측정 지적 년 월 일
											점사 지적 년 월 일

측량준비도	측량결과도	측량 성확도	도 면
작성	확인	작성	정리
			점사
측량	년 월 일	팀장 지적	④
		팀원 지적	④
		팀원 지적	④
점사	년 월 일	지적	시군구 ④

기준점 번호 및 거리 방위각 좌표 기재

측정면적, 보정면적은 셋째자리, 산출면적은 정계점좌표등록부 지역,1/600 지역은 둘째자리,
그 밖의 지역은 첫째자리까지, 결정면적은 등록단위까지 입력


4. 분할측량결과도(1200 분의 1 지역)

42750250240111271000139040420070431.dat



용인시 처인구 운학동 분할측량결과도 제 2254 호 (지적도 제 9 호) 측척 1200 분의 1
접수일 : 〇〇년 〇〇월 〇〇일 (〇〇 필)

(0.0)	신측량	용도지역
(0.0)	도라산측	0.0
(0.0)	보정계수	〇〇〇지역
(0.0)	1.0000	

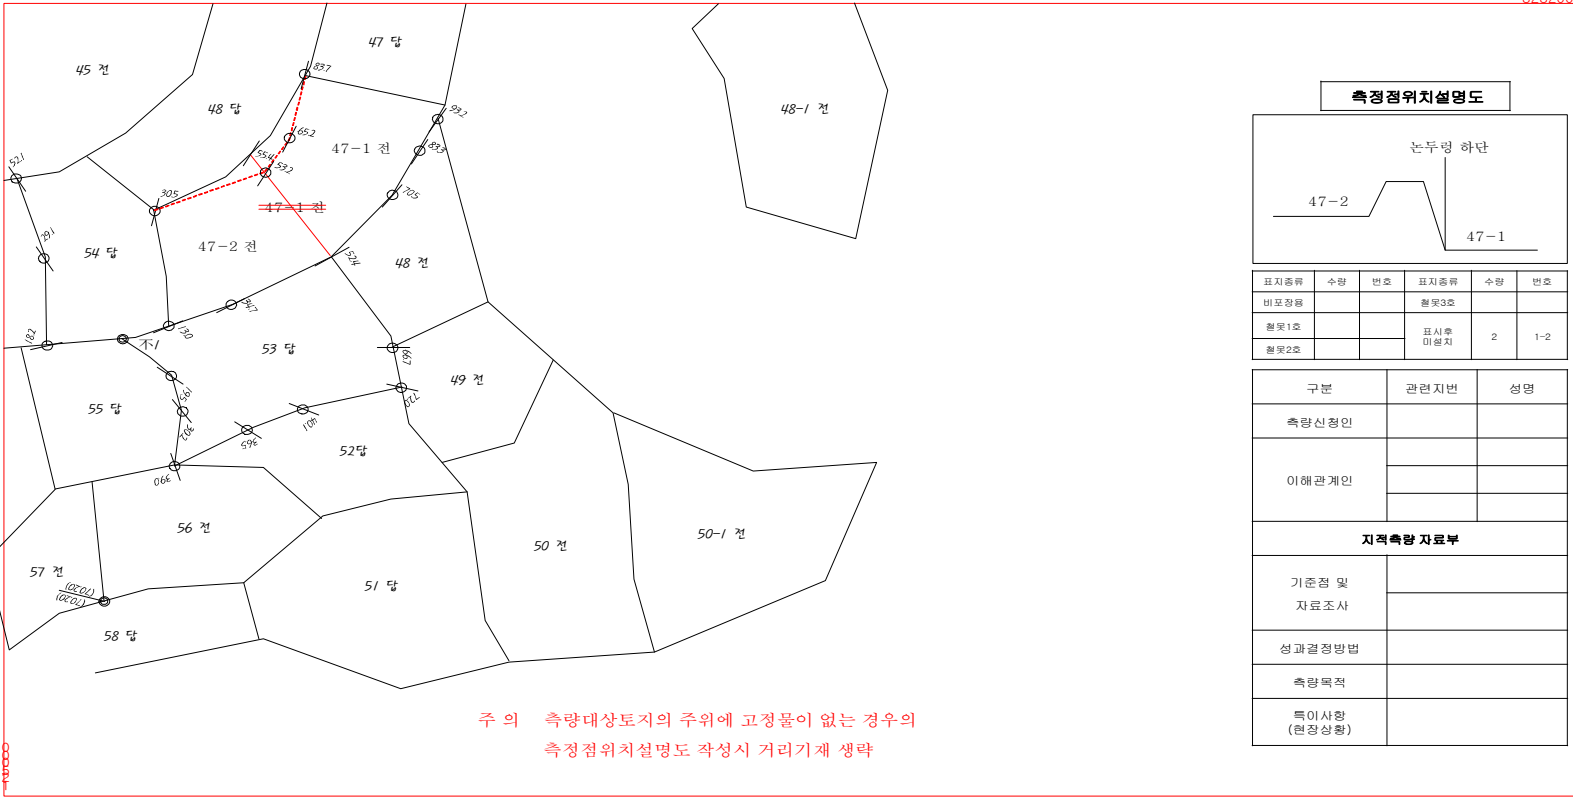


주의 측량대상토지의 주위에 고정물이 없는 경우의
측정점위치설명도 작성시 거리기재 생략

322800

지적측량 기준점 번호	거리	방위각	좌표
	m	° ' "	X Y

동리명	지번	측정 방법	회수 및 산출수		측정면적	도라산측 보정계수	보정면적	원면적	산출면적	결정면적	비고
			제 1 회	제 2 회							
운학	47-1	전자	638.368	638.368	638.368				638.9	634	
	47-2	전자	620.472	620.472	620.472				616.1	616	
	47-1				1258.840			1250	1250.0	1250	측정 지력
											년 월 일
											년 월 일
											년 월 일
											년 월 일
											년 월 일
											년 월 일
											년 월 일

측정면적, 보정면적은 셋째자리, 산출면적은 경계점좌표등록부 지역,1/600 지역은 둘째자리,
그 밖의 지역은 첫째자리까지, 결정면적은 등록단위까지 입력

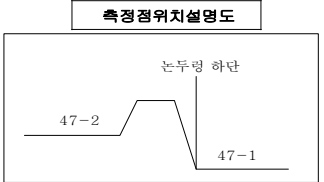

표지종류	수량	번호	표지종류	수량	번호
비표장용			표지종류		
표지1호			표지2호		
표지2호			표지3호		


구분	관련지번	성명
측량신청인		
이해관계인		

지적측량 자료부	
기준점 및 자료조사	
성과결정방법	
측량목적	
특이사항 (현장상황)	

측량준비도	측량결과도	측량 성과도	도면
작성	확인	작성	확인


측량 년 월 일
검사 년 월 일
팀장 지력
팀원 지력
팀원 지력
시군구

42750250240111271000139040420070431.dat

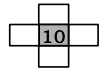

용인 시 처인 구 운학 동 분할 측량결과도(좌표) 제 954 호 (지적도 제 10 호) 축척 500 분의 1
접수일: 〇〇년 〇〇월 〇〇일 (〇〇 필)

(0.0)	신축량	용도지역 ○○○지역
(0.0) 도곽신축 (0.0)	mm 0.0	
(0.0)	보정계수	
	1.0000	

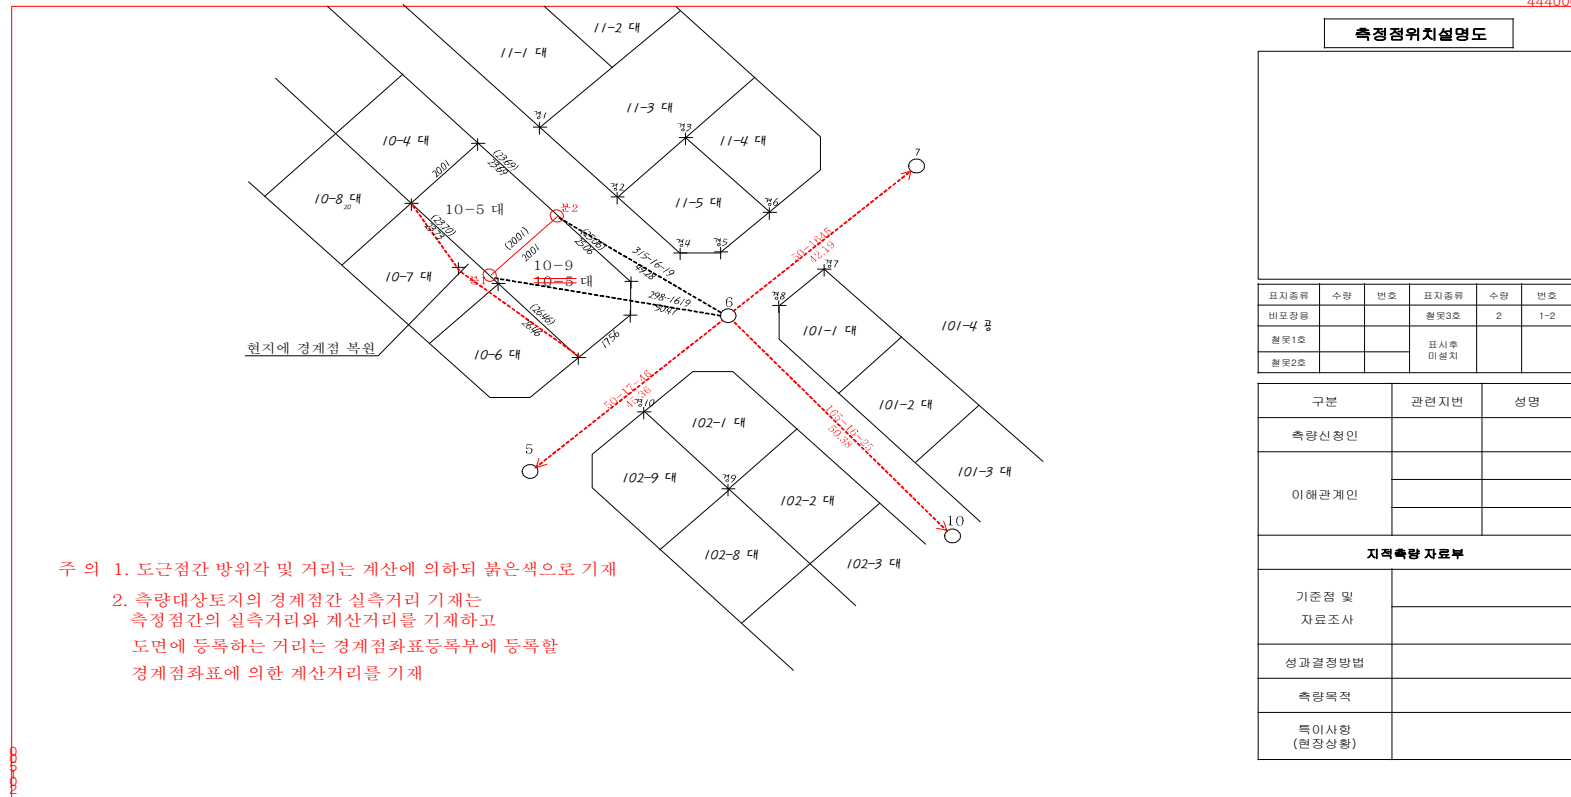[illegible][illegible]

측량준비도		측량결과도			측량 성적도 작성	도 면	
작성	확인	작성	확인	검사		정리	검사
측량 년 월 일 팀장 지적 팀원 지적 팀원 지적 검사 년 월 일 지적 시 군 구							


기준점 번호 및 거리 방위각 좌표 기재

측정면적, 보정면적은 셋째자리, 산출면적은 경계점좌표등록부 지역,1/600 지역은 둘째자리,
그 밖의 지역은 첫째자리까지, 결정면적은 등록단위까지 입력

42750250240111271000139040420070431.dat

용인 시 처인 구 운학 동 분할측량결과도(좌표) 제 496 호 (지적도 제 18 호) 축척 500 분의 1
접수일: 〇〇년 〇〇월 〇〇일 (〇〇 필)

용도지역	상업지역
------	------

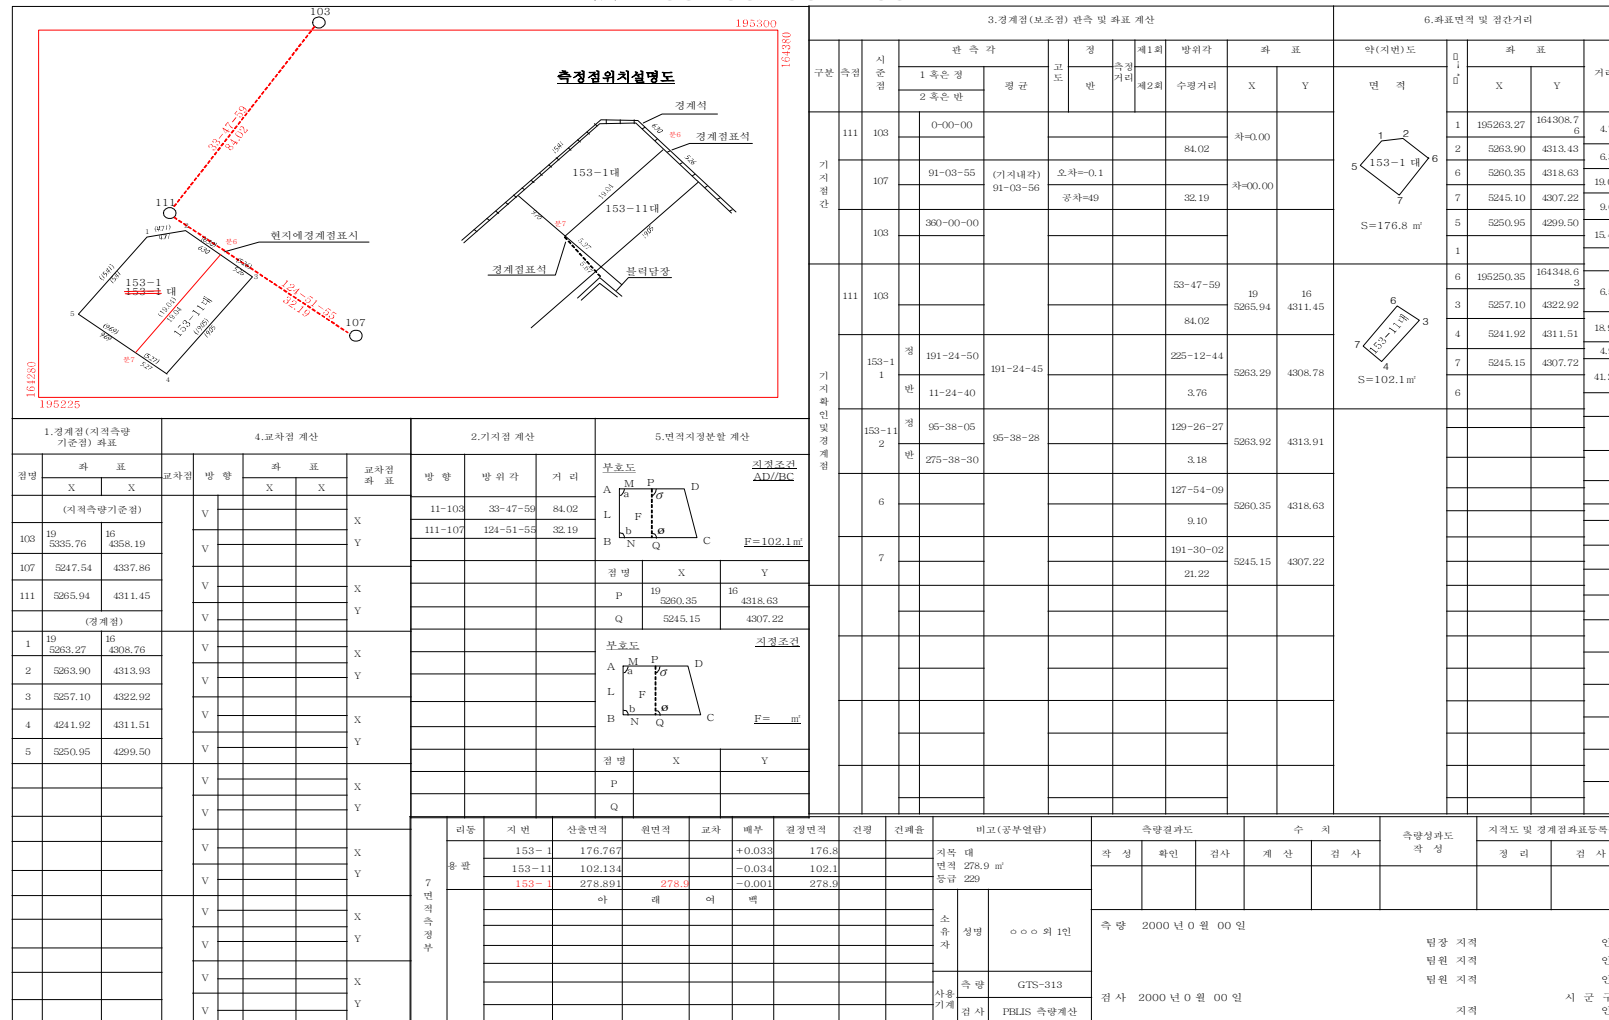


7. 경계복원측량결과도 (1200분의 1)



용인시 처인구 운학동 경계복원측량결과도 제 1664 호 (지적도 제 9 호) 축척 1200 분의 1
접수일: 00년 00월 00일 (00 필)


(0.0)	신축방	용도지역
(0.0)	도곽선축	○○○지역
(0.0)	보경계수	1.0000

323200

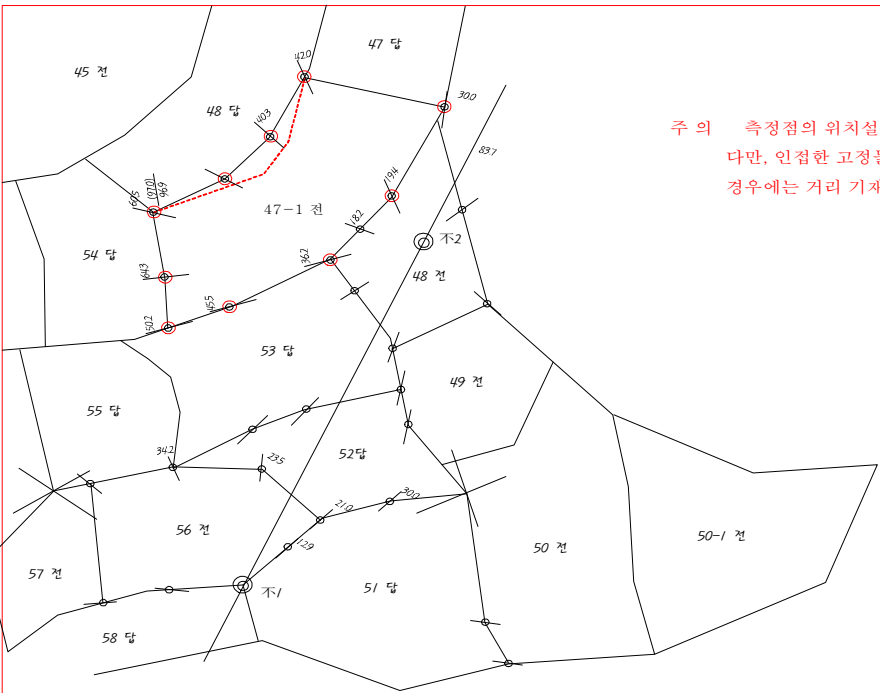

주의 측점점의 위치설명도(3방향이상의 주위 고정물로부터 거리) 기재.
다만, 인접한 고정물 없는 경우와 연속지, 집단지 등 대단위 업무의
경우에는 거리 기재를 생략한다.

측점점위치설명도

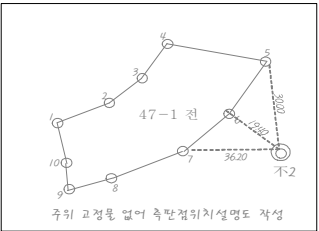

표지종류	수량	번호	표지종류	수량	번호
비포장길	10	1-10	불못3호		
불못1호			표시후 미설치		
불못2호					

구분	관련지번	성명
측량신청인		
이해관계인		

지적측량 자료부

기준점 및 자료조사	
성과결정방법	
측량목적	
특이사항 (현장상황)	

322800

지적측량 기준점 번호	거리	방위각	좌 X	표 Y
	mm	도 / 분 / 초	mm	mm
	-	-	-	-
	-	-	-	-
	-	-	-	-

지적측량 기준점 번호	거리	방위각	좌 X	표 Y
	mm	도 / 분 / 초	mm	mm
	-	-	-	-
	-	-	-	-
	-	-	-	-

측량준비도		측량결과도			측 량 성 과 도 작 성
작성	확인	작성	확인	검사	


측량 년 월 일

팀장 지적 인
팀원 지적 인
팀원 지적 인

8. 경계복원측량결과도(좌표)

용인 시 처인 구 운학 동 경계복원 측량결과도(좌표) 제 64 호 (지적도 제 8 호) 축척 500 분의 1
접수일 : 00년 00월 00일 (00 필)

(0.0)	신축방향	용도지역
(0.0)	도락신축	○○○지역
(0.0)	보정계수	1.0000

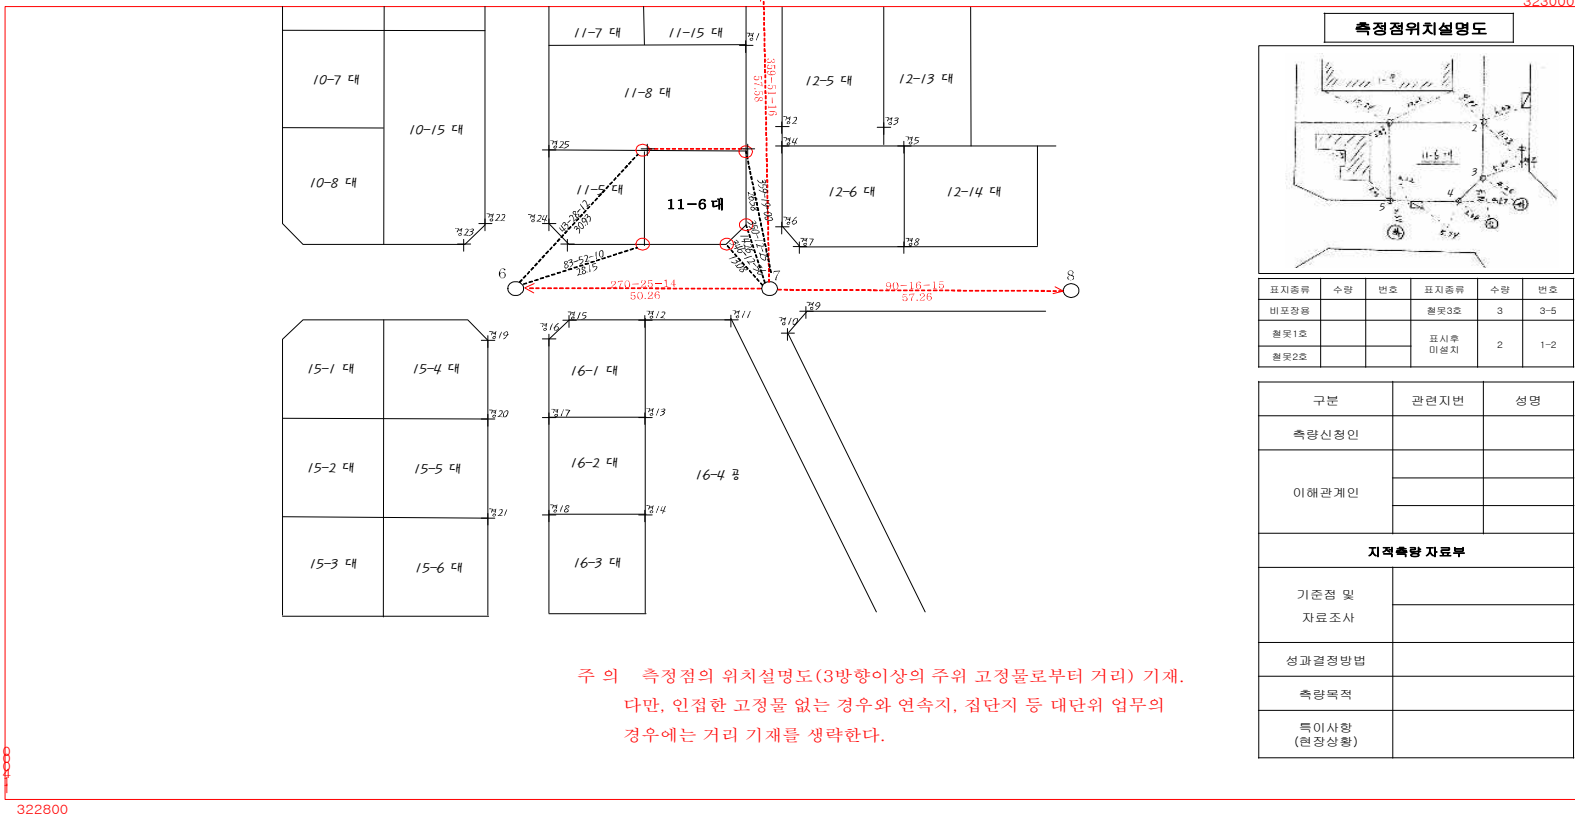

측정점위치설명도

표지종류	수량	번호	표지종류	수량	번호
비포장도로			철도3호	3	3-5
철도1호			표지종류		
철도2호			미설치	2	1-2

구분	관련지번	성명
측량신청인		
이해관계인		

지적측량 자료부

기준점 및 자료조사	
성과결정방법	
측량목적	
특이사항 (현장상황)	

지적측량 기준점 번호	거리	방위각	좌 X	표 Y
1	...	...	...	...
2	...	...	...	...
3	...	...	...	...
4	...	...	...	...


지적측량 기준점 번호	거리	방위각	좌 X	표 Y
5	...	...	...	...
6	...	...	...	...
7	...	...	...	...
8	...	...	...	...

측량준비도		측량결과도			측 량 성 과 도 작 성
작성	확인	작성	확인	검사	

측량 년 월 일 팀장 지적 인
팀원 지적 인
팀원 지적 인

90

용도지역	주거지역
------	------

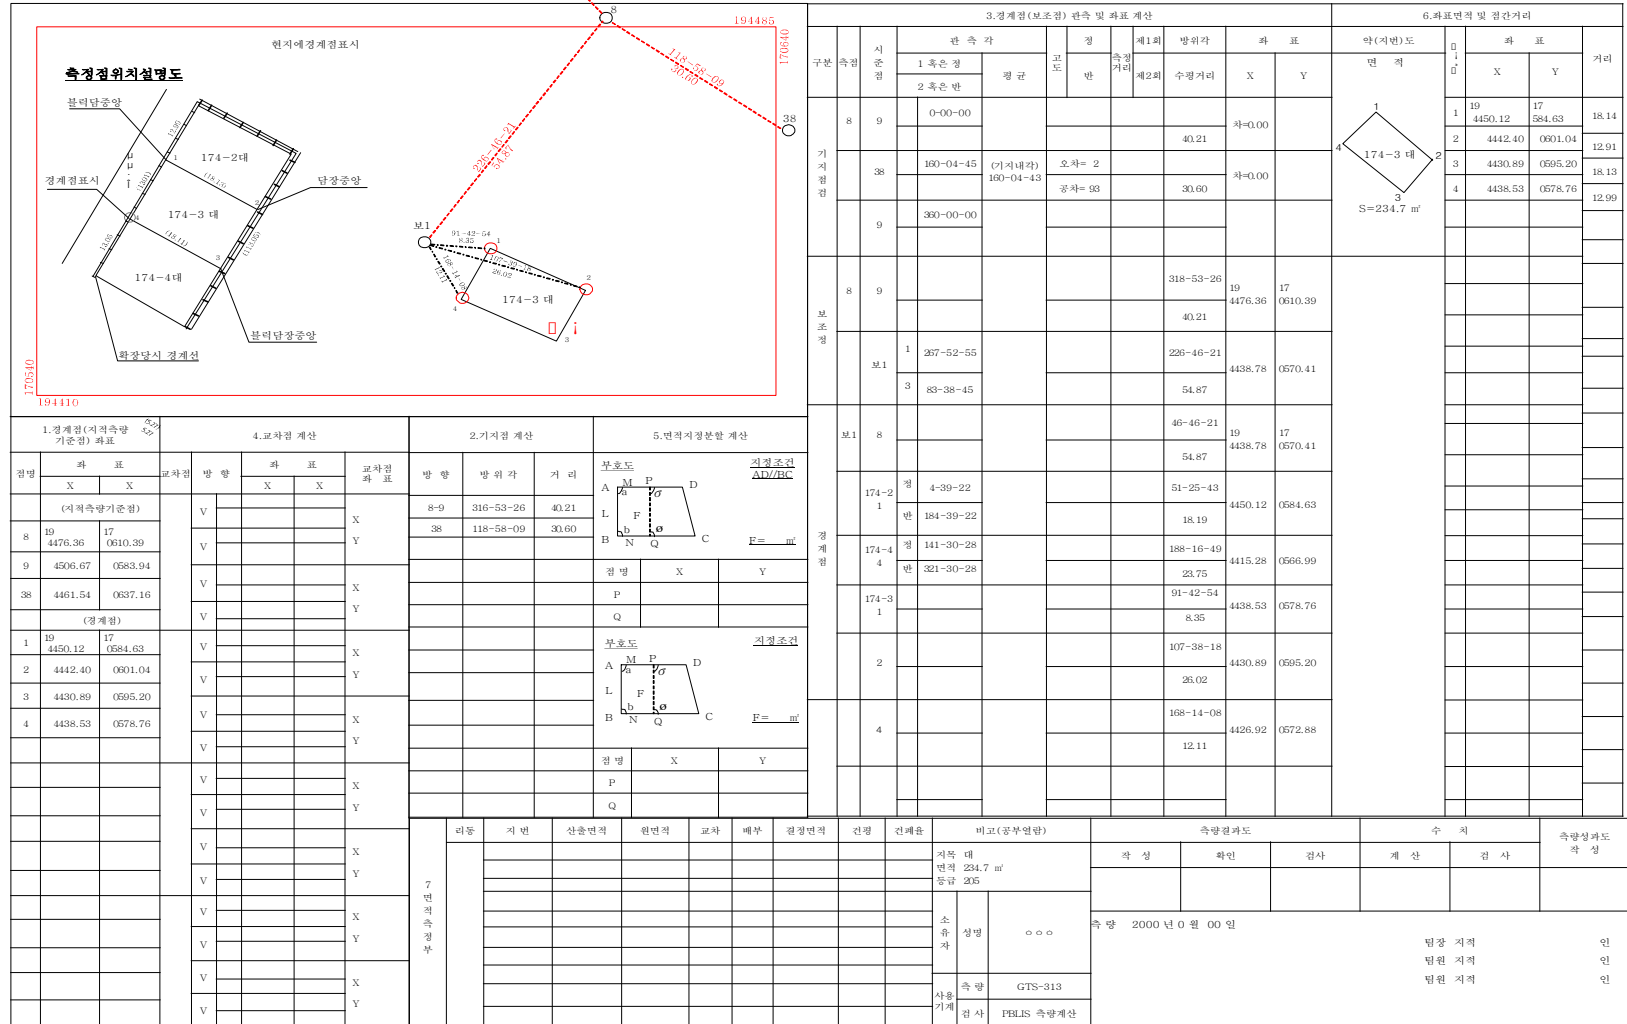


10. 지적확정측량결과도(경위의측량방법으로세부측량을한지역)

42750250240111271000139040420070431.dat



용인시 운학동 지적확정 측량결과도 제 3 호 축척 500 분의 1

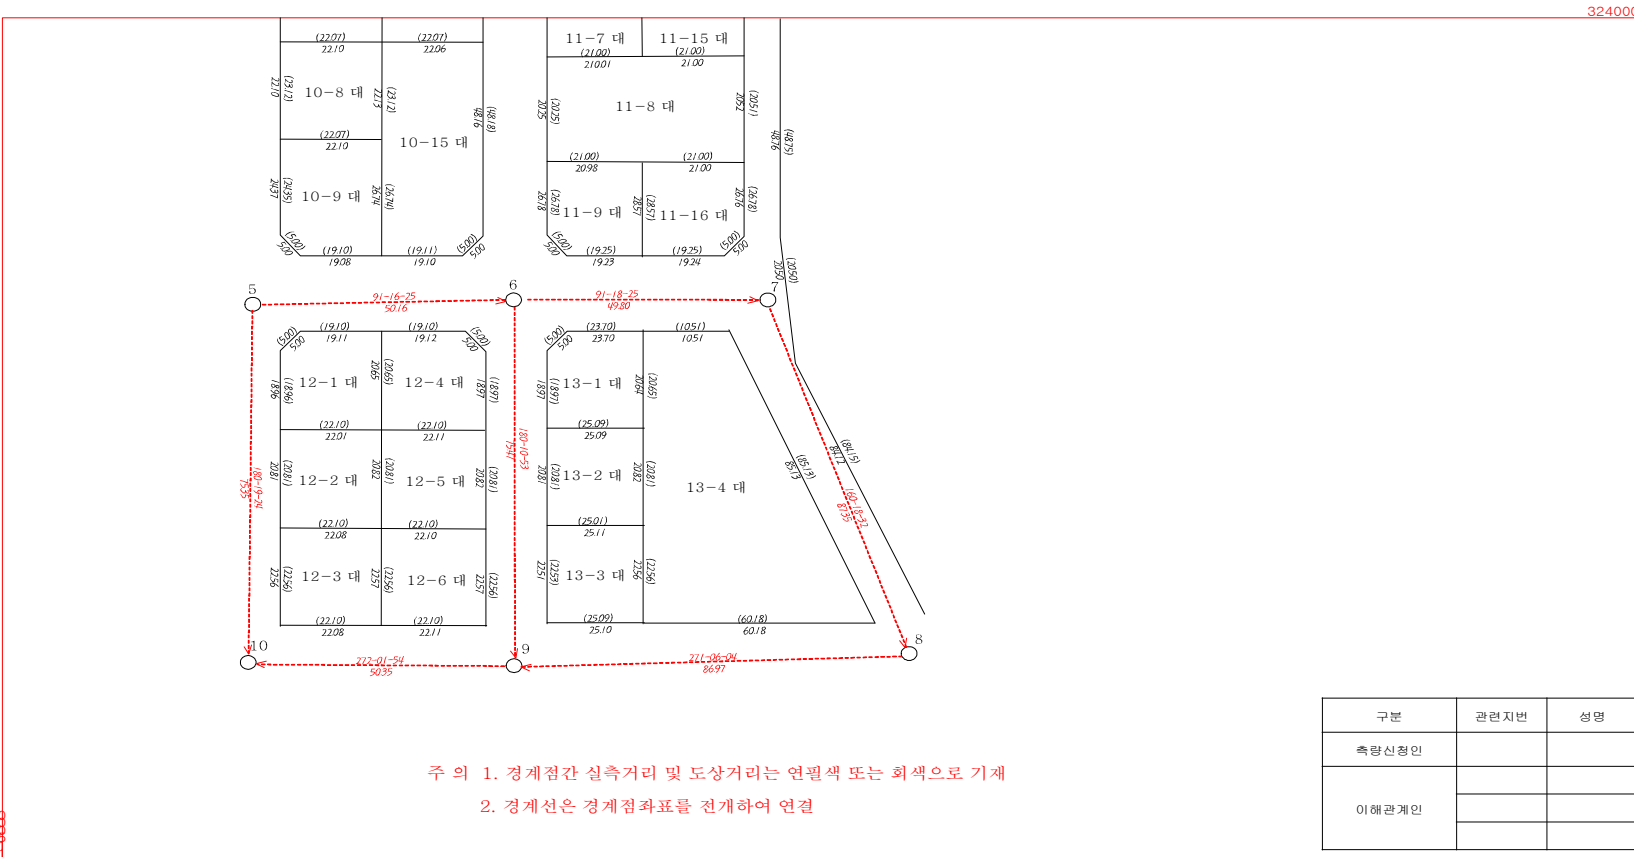

주 의 1. 경계점간 실측거리 및 도상거리는 연필색 또는 회색으로 기재
2. 경계선은 경계점좌표를 전개하여 연결

구분	관련지번	성명
측량신청인		
이해관계인		

323850		지적측량 기준점 번호		거리	방위각	좌 표		지적측량 기준점 번호		거리	방위각	좌 표		측량준비도		측량결과도		측량 성파도 작성		측량 년 월 일		필장 지적		인
						X						X		작성		확인						필원 지적		인
																						필원 지적		인
																						시·군·구		인
																						지적		인

11. 지적재산파일에 의한 측량결과도(분할측량)

용인시 처인구 운학동 분할측량결과도 제 2254 호 (지적도 제 9 호) 축척 1200 분의 1

접수일 : ○○년 ○○월 ○○일 (○○ 필)

	신축량	용도지역 ○○○지역
	mm 0.0	
	보정계수	
	1.0000	



322800					
계리측량 기준점 번호	거리	방위각	좌 표		
			X	Y	
1	90°21'	-25-49"	322843.00	125032.96	
2	90°21'	-25-49"	322851.56	125032.96	
3	88°55'	88-38'-37"	322854.00	12515.88	
	.	.	.	.	
	.	.	.	.	
	.	.	.	.	
	.	.	.	.	
	.	.	.	.	
	.	.	.	.	
	.	.	.	.	

동리명	지번	측정방법	회수 및 산출수		측정면적	도락신축보정계수	보정면적	원면적	산출면적	결정면적	비고
			제 1 회	제 2 회							
윤학	47-1	전상	256.712	256.712	256.712		m²	m²	255.7	256	측정지력 년 월 일 ⑨ 검사지력 년 월 일 ⑩
	47-2	전상	246.321	246.321	246.321				245.3	245	
	47-1				503.033				501.0	501	
					아 래 빈 칸						

측량준비도		측량결과도		측량 성라도 작성	도 면	
작성	확인	작성	확인		검사	검사
측량 년 월 일				팀장 지력 팀원 지력 팀원 지력 지력	시 군 구	⑨ ⑩ ⑪
검사 년 월 일						

기준점 번호 및 거리 방위각 좌표 기재

측정면적, 보정면적은 셋째자리, 산출면적은 경계점좌표등록부 지역,1/600 지역은 둘째자리,
그 밖의 지역은 첫째자리까지, 결정면적은 등록단위까지 입력

12. 지적전산파일에 의한 측량결과도(경계복원측량)




용인시 처인구 운학동 경계복원 측량결과도 제 2254 호 (지적도 제 9 호) 축척 1200 분의 1
접수일 : 00년 00월 00일 (00월)

전자평판측량


(0.0)	신축량	용도지역
(0.0) 도박신축 (0.0)	0.0	000지역
(0.0)	보정계수	1.0000

323200

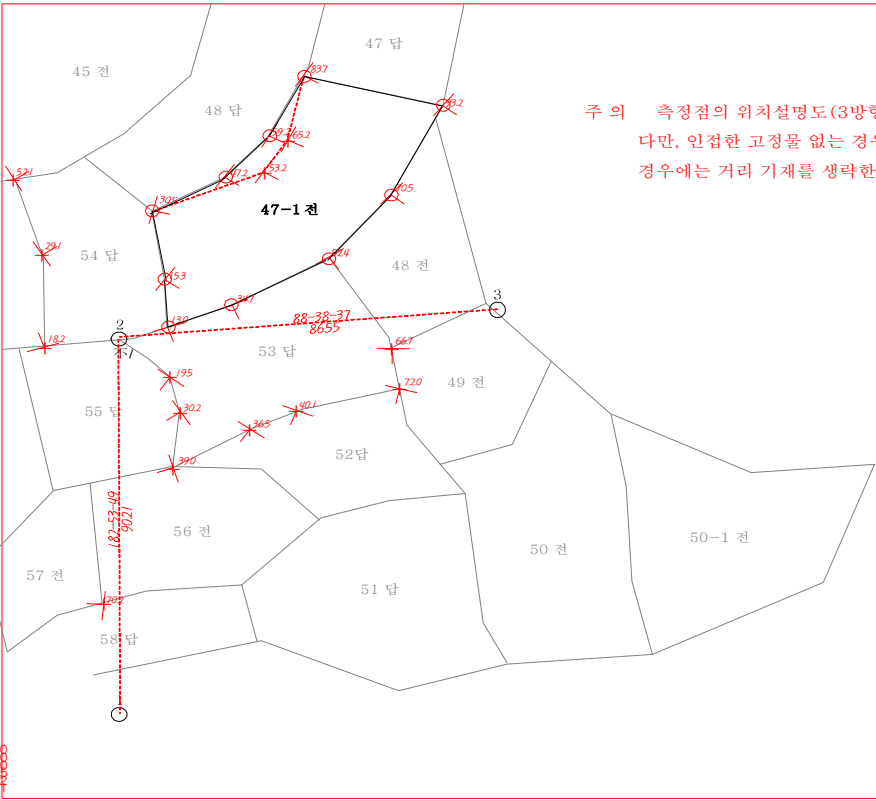

주의 측정점의 위치설명도(3방향이상의 주위 고정물로부터 거리) 기재.
다만, 인접한 고정물 없는 경우와 연속지, 집단지 등 대단위 업무의
경우에는 거리 기재를 생략한다.

측정점위치설명도

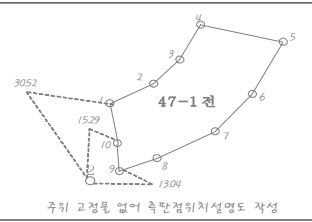

표지종류	수량	번호	표지종류	수량	번호
비표장물	10	1-10	물못3호		
물못1호			표시후 미설치		
물못2호					

구분	관련지번	성명
측량신청인		
이해관계인		

지적측량 자료부

기준점 및 자료조사	00년 00월 00일 00시 00분 정확도 도근 사용 00년 00월 00일 측량결과도(점 수번호 00 호 00번지) 참조
성과결정방법	기준점 성과에 의함
측량목적	등록전환을 위한 임야분할
특이사항 (현장상황)	

322800

지적측량 기준점 번호	거리	방위각	좌표	
			X	Y
1			322846.00	125032.66
2	90.21	2-53-49	322851.56	125033.90
3	86.55	88-36-37	322854.00	125115.86

기준점 번호 및 거리 방위각 좌표 기재

지적측량 기준점 번호	거리	방위각	좌표	
			X	Y

측량준비도		측량결과도			측량 성과도 작성
작성	확인	작성	확인	점사	

측량 년 월 일 팀장 지적 인
팀원 지적 인
팀원 지적 인