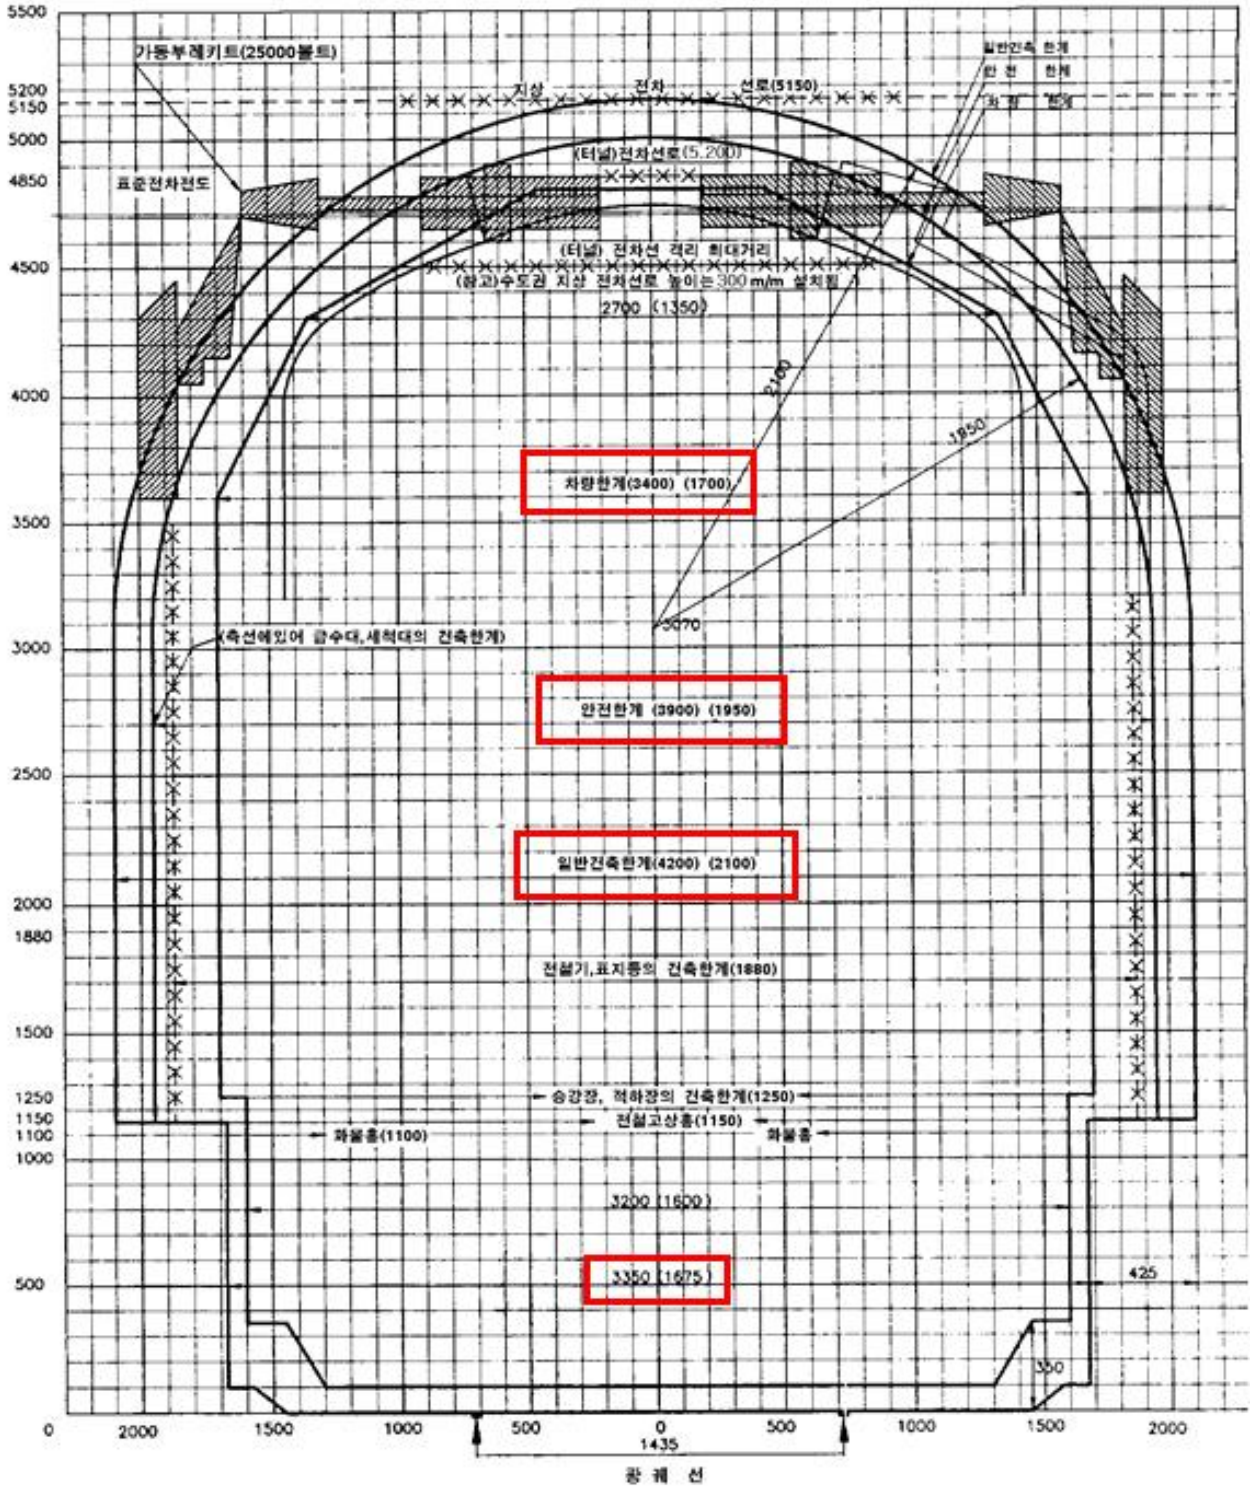[별표 2] 화차 차량한계도 및 일반건축한계도(제8조 관련)